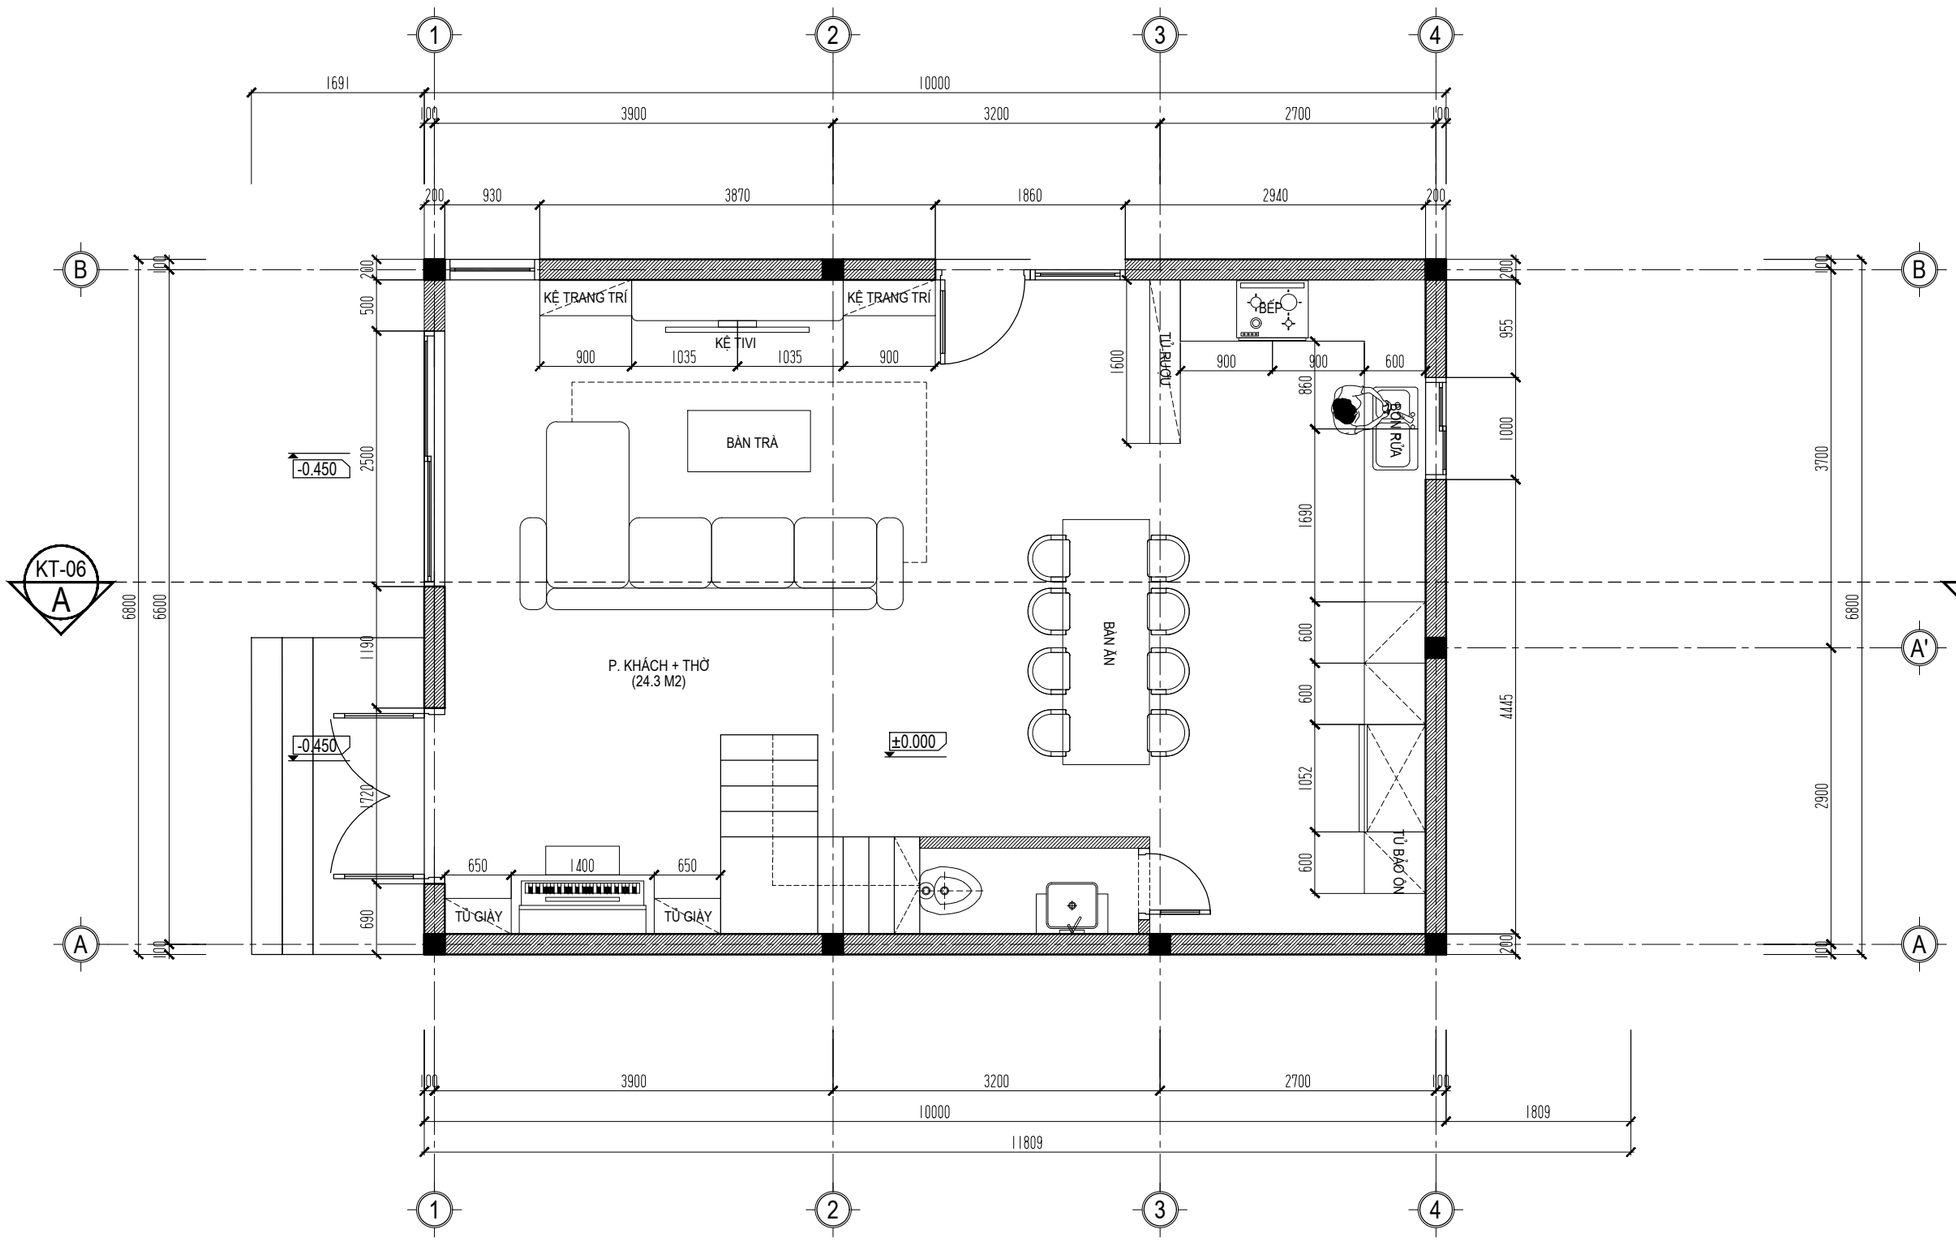


MẶT BẰNG TẦNG 1

SCALE 1:60

ĐƠN VỊ TƯ VẤN THIẾT KẾ - DESIGNED BY :

NOU.DESIGN

HOTLINE: 0963. 653. 568 - 0911.176. 222
VĂN PHÒNG: M01- L16 KĐT DƯƠNG NỘI
HÀ ĐÔNG - HÀ NỘI
EMAIL: NOUDESIGN.INTERIOR@GMAIL.COM
XƯỞNG SẢN XUẤT: KM19 - ĐƯỜNG 32
ĐỨC THƯỢNG - HOÀI ĐỨC - HÀ NỘI

CHỦ ĐẦU TƯ - PROJECT OWNER :

NGUYỄN NHẬT MINH

TÊN CÔNG TRÌNH - PROJECT

NHÀ Ở

HẠNG MỤC - PROJECT

XÂY MỚI

VỊ TRÍ - LOCATION

THỬA ĐẤT SỐ : 109, TỜ BẢN ĐỒ SỐ : 53
TỔ 4, P. NGỌC THỤY
Q. LONG BIÊN, TP. HÀ NỘI

GIÁM ĐỐC - DIRECTOR

ĐẶNG MINH ĐỨC

CHỦ TRÌ - PRIMARY ARCHITECT

TRẦN ĐỨC NGHĨA

KIỂM TRA / CHECKED BY

NGUYỄN PHƯƠNG THẢO


THIẾT KẾ / DESIGNED BY

NGUYỄN ĐĂNG KHOA

TÊN BẢN VẼ - DRAWING NAME

MẶT BẰNG TẦNG 1

TỶ LỆ	BẢN VẼ SỐ - DRAWING NO
	KT- 01
NGÀY HOÀN THÀNH (DATE OF ISSUE)	DD/MM/-------

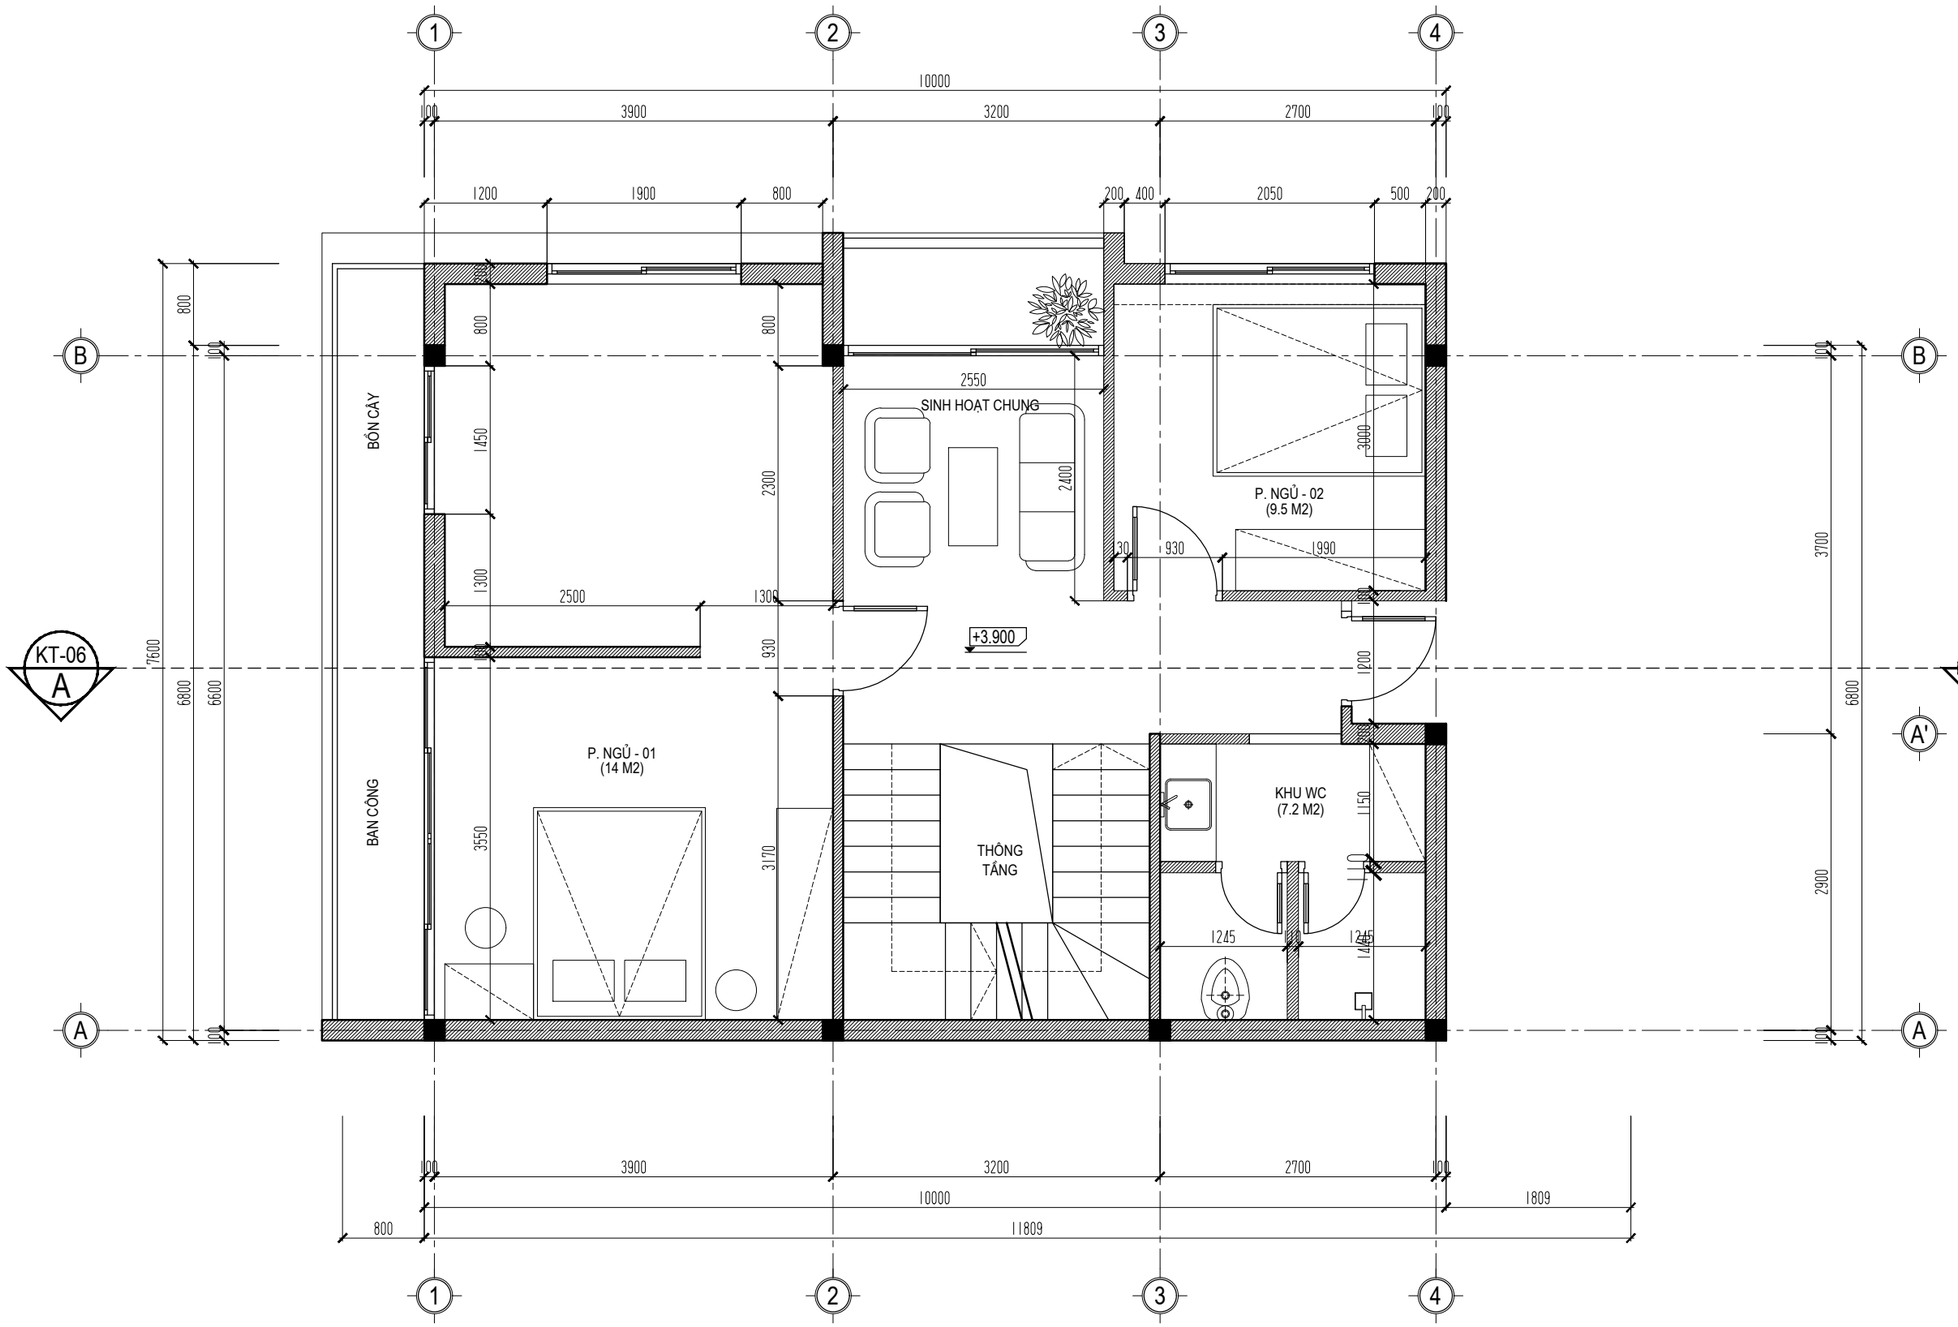

MẶT BẰNG TẦNG 2

SCALE 1:60

ĐƠN VỊ TƯ VẤN THIẾT KẾ - DESIGNED BY :

NOU.DESIGN

HOTLINE: 0963. 653. 568 - 0911.176. 222
VĂN PHÒNG: M01- L16 KĐT DƯƠNG NỘI
HÀ ĐÔNG - HÀ NỘI
EMAIL: NOUDESIGN.INTERIOR@GMAIL.COM
XƯỞNG SẢN XUẤT: KM19 - ĐƯỜNG 32
ĐỨC THƯỢNG - HOÀI ĐỨC - HÀ NỘI

CHỦ ĐẦU TƯ - PROJECT OWNER :

NGUYỄN NHẬT MINH

TÊN CÔNG TRÌNH - PROJECT

NHÀ Ở

HẠNG MỤC - PROJECT

XÂY MỚI

VỊ TRÍ - LOCATION

THỬA ĐẤT SỐ : 109, TỜ BẢN ĐỒ SỐ : 53
TỔ 4, P. NGỌC THỤY
Q. LONG BIÊN, TP. HÀ NỘI

GIÁM ĐỐC - DIRECTOR

ĐẶNG MINH ĐỨC

CHỦ TRÌ - PRIMARY ARCHITECT

TRẦN ĐỨC NGHĨA

KIỂM TRA / CHECKED BY

NGUYỄN PHƯƠNG THẢO


THIẾT KẾ / DESIGNED BY

NGUYỄN ĐĂNG KHOA

TÊN BẢN VẼ - DRAWING NAME

MẶT BẰNG TẦNG 2

TỶ LỆ	BẢN VẼ SỐ - DRAWING NO
	KT- 02
NGÀY HOÀN THÀNH (DATE OF ISSUE)	DD/MM/-------

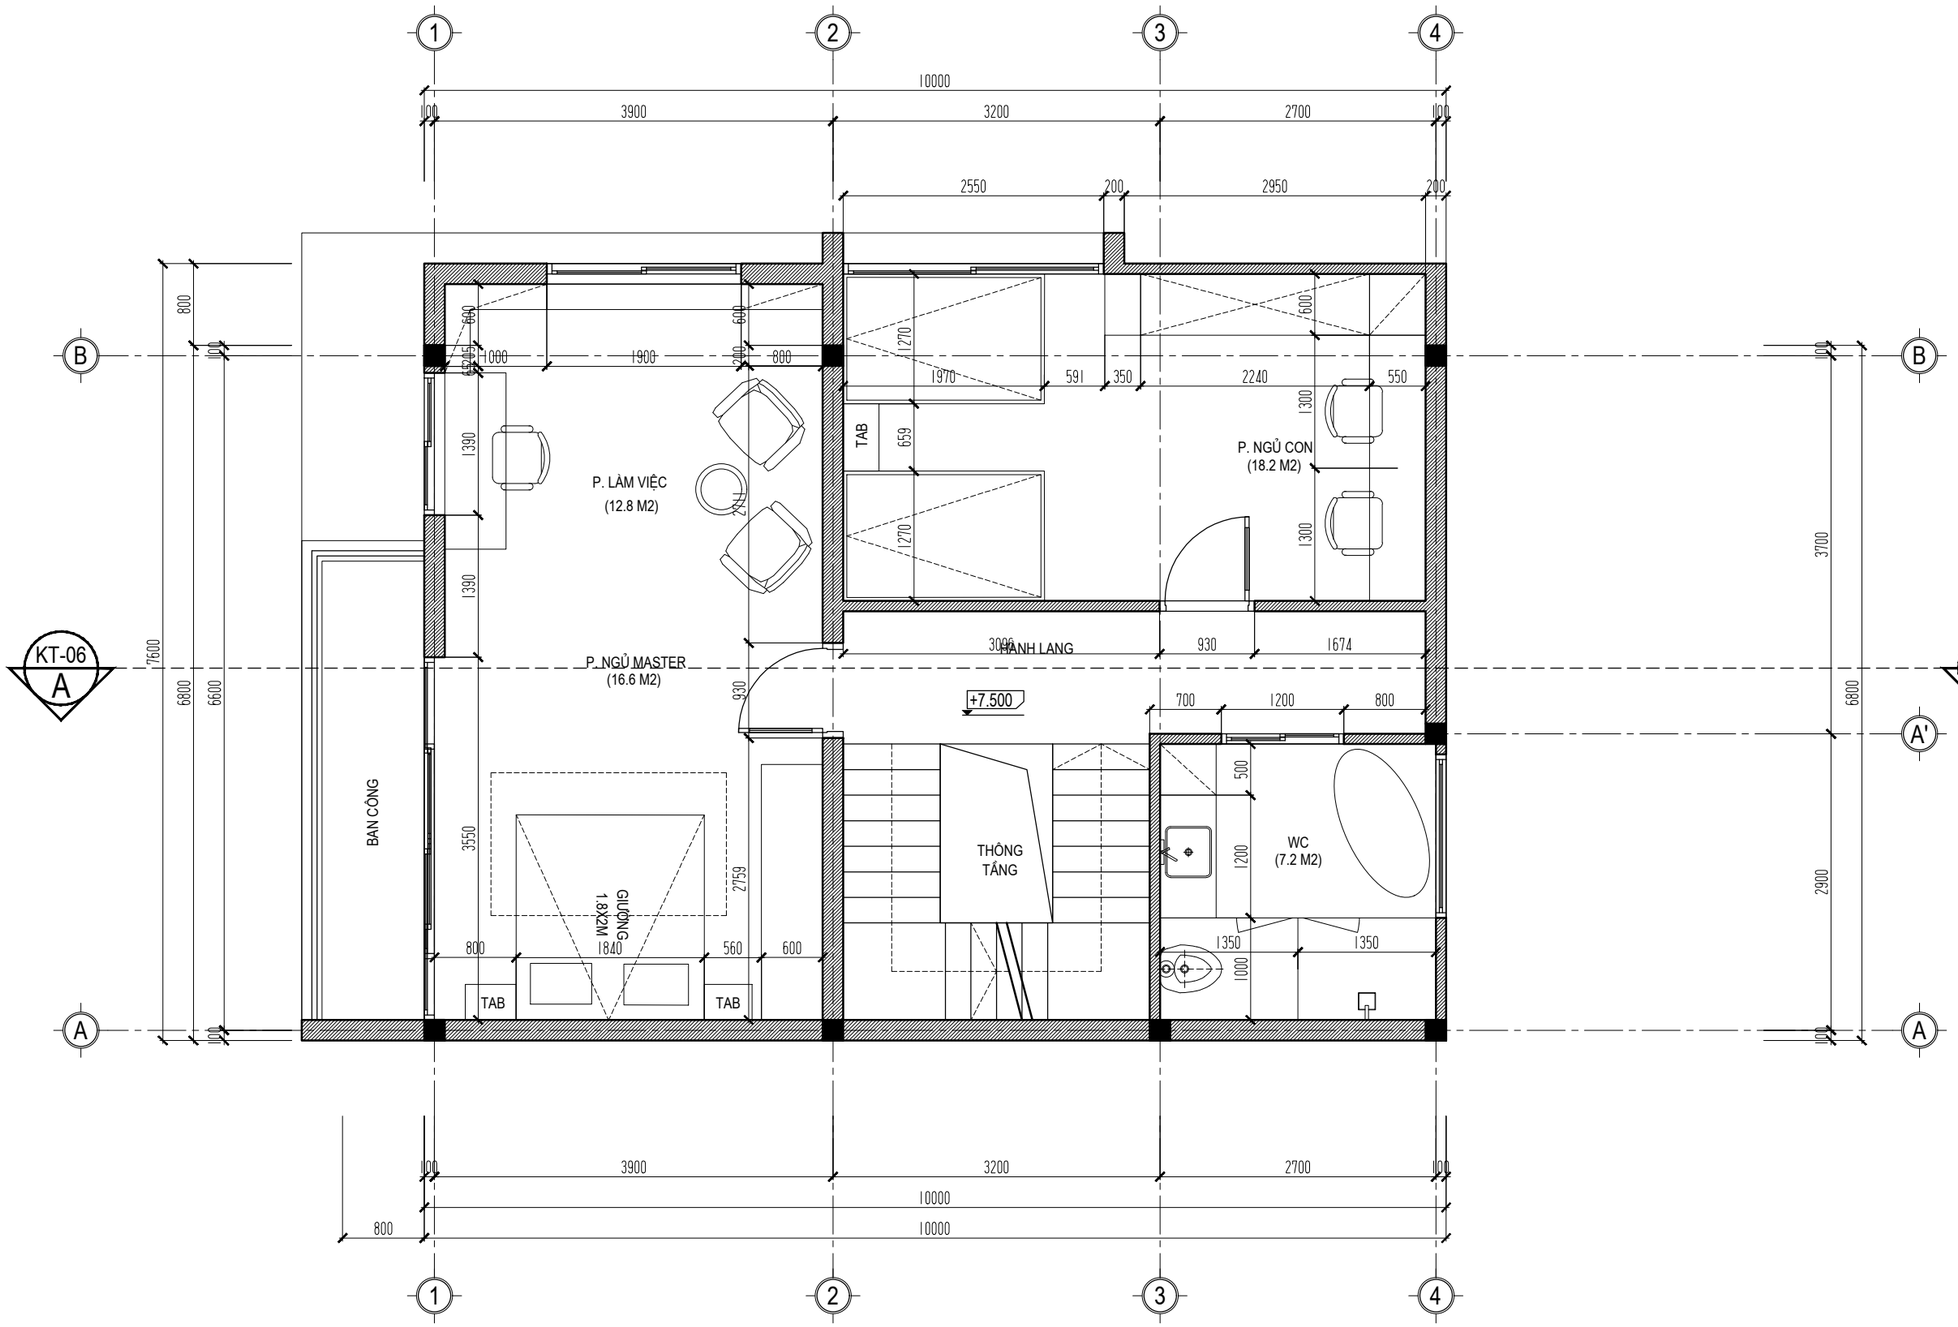

MẶT BẰNG TẦNG 3

SCALE 1:60

ĐƠN VỊ TƯ VẤN THIẾT KẾ - DESIGNED BY :

NOU.DESIGN

HOTLINE: 0963. 653. 568 - 0911.176. 222
VĂN PHÒNG: M01- L16 KĐT DƯƠNG NỘI
HÀ ĐÔNG - HÀ NỘI
EMAIL: NOUDESIGN.INTERIOR@GMAIL.COM
XƯỞNG SẢN XUẤT: KM19 - ĐƯỜNG 32
ĐỨC THƯỢNG - HOÀI ĐỨC - HÀ NỘI

CHỦ ĐẦU TƯ - PROJECT OWNER :

NGUYỄN NHẬT MINH

TÊN CÔNG TRÌNH - PROJECT

NHÀ Ở

HẠNG MỤC - PROJECT

XÂY MỚI

VỊ TRÍ - LOCATION

THỬA ĐẤT SỐ : 109, TỜ BẢN ĐỒ SỐ : 53
TỔ 4, P. NGỌC THỤY
Q. LONG BIÊN, TP. HÀ NỘI

GIÁM ĐỐC - DIRECTOR

ĐẶNG MINH ĐỨC

CHỦ TRÌ - PRIMARY ARCHITECT

TRẦN ĐỨC NGHĨA

KIỂM TRA / CHECKED BY

NGUYỄN PHƯƠNG THẢO


THIẾT KẾ / DESIGNED BY

NGUYỄN ĐĂNG KHOA

TÊN BẢN VẼ - DRAWING NAME

MẶT BẰNG TẦNG 3

TỶ LỆ	BẢN VẼ SỐ - DRAWING NO
	KT- 03
NGÀY HOÀN THÀNH (DATE OF ISSUE)	DD/MM/-------

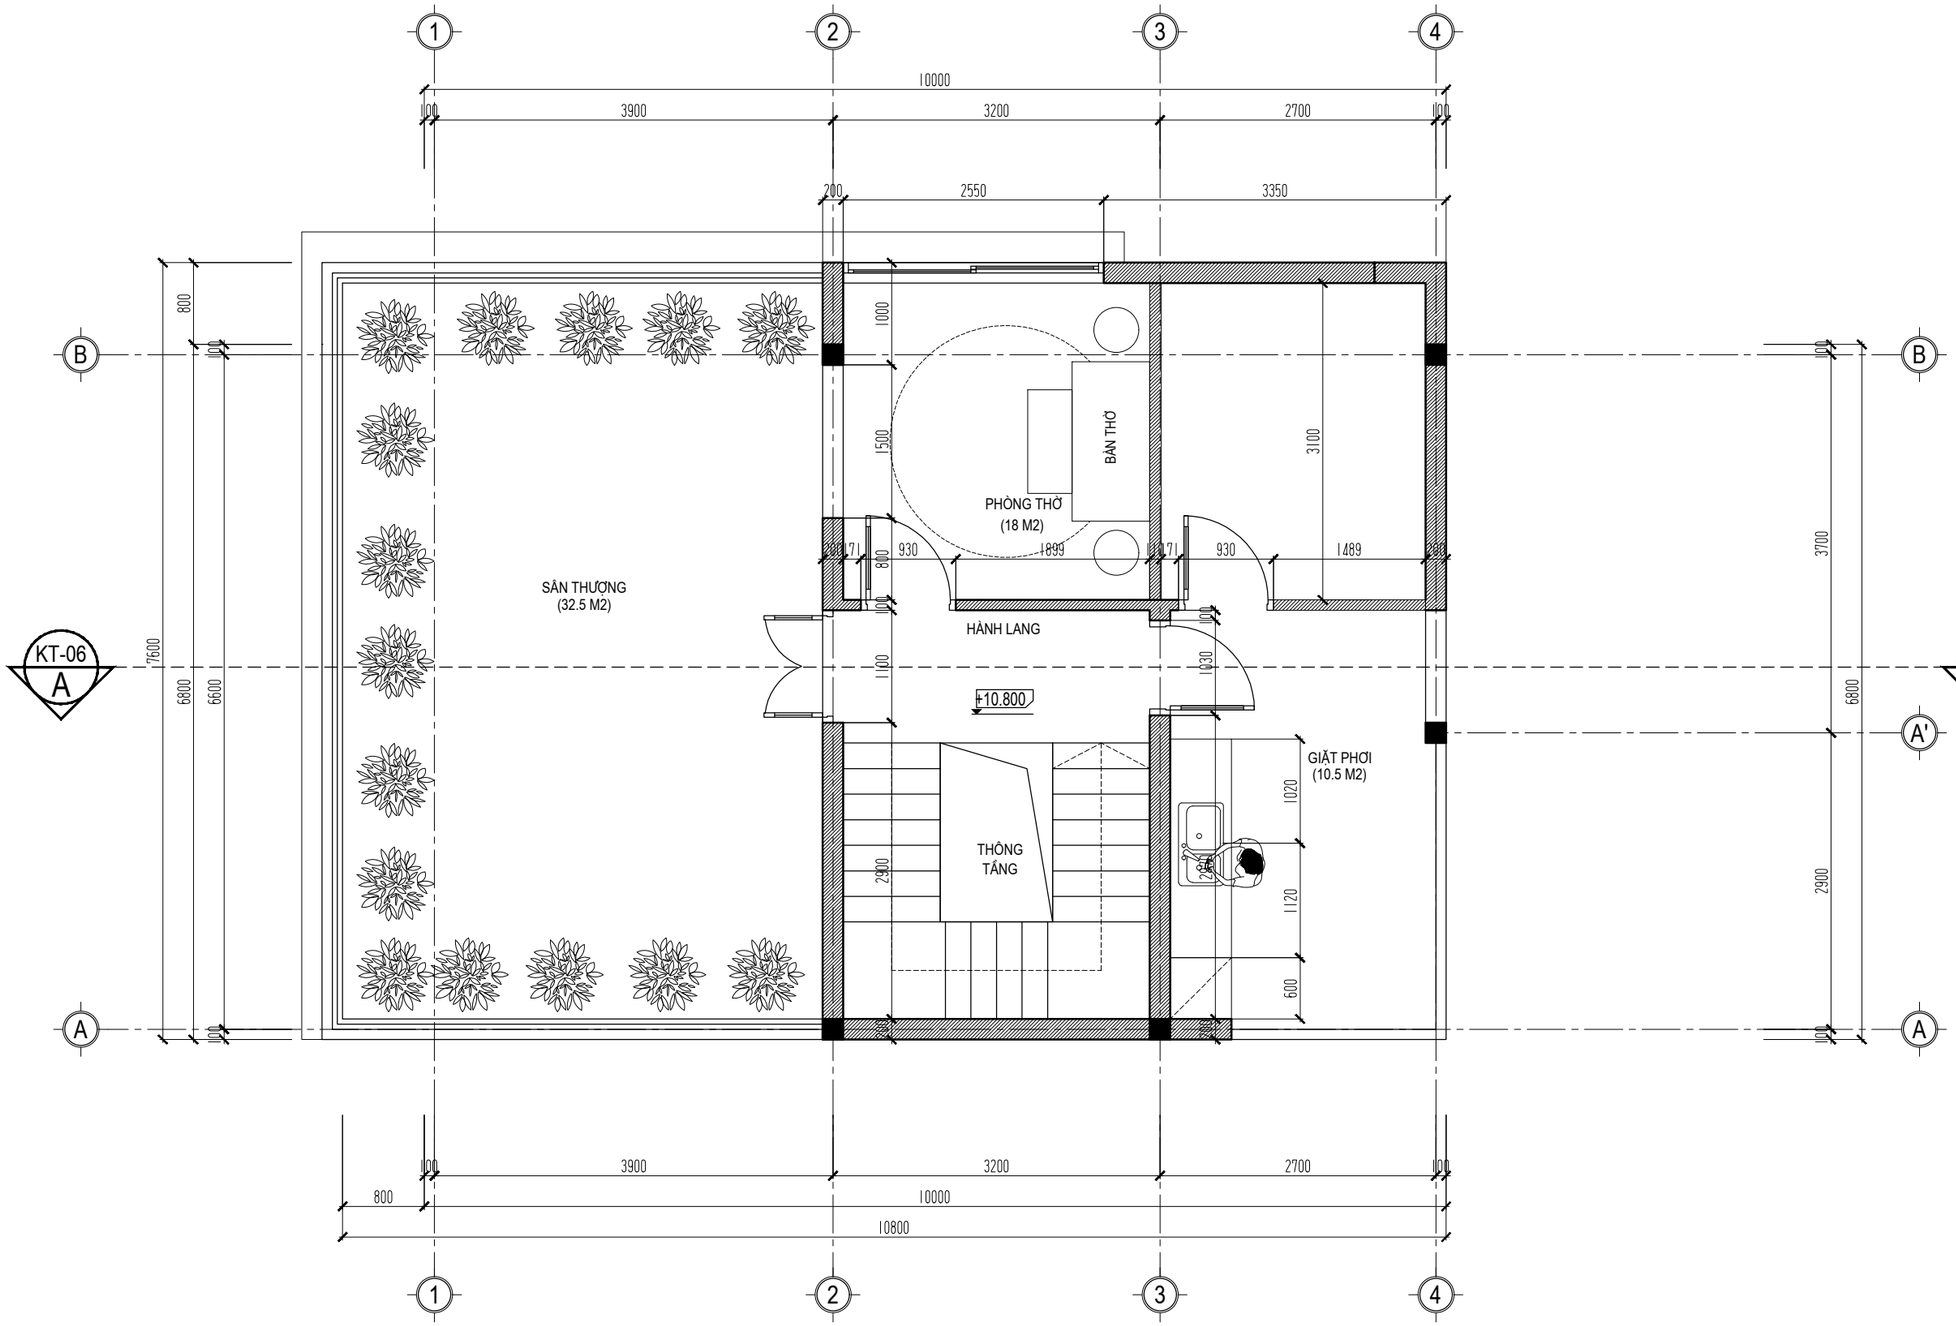

MẶT BẰNG TẦNG TUM

SCALE 1:60

ĐƠN VỊ TƯ VẤN THIẾT KẾ - DESIGNED BY :

NOU.DESIGN

HOTLINE: 0963. 653. 568 - 0911.176. 222
VĂN PHÒNG: M01- L16 KĐT DƯƠNG NỘI
HÀ ĐÔNG - HÀ NỘI
EMAIL: NOUDESIGN.INTERIOR@GMAIL.COM
XƯỞNG SẢN XUẤT: KM19 - ĐƯỜNG 32
ĐỨC THƯỢNG - HOÀI ĐỨC - HÀ NỘI

CHỦ ĐẦU TƯ - PROJECT OWNER :

NGUYỄN NHẬT MINH

TÊN CÔNG TRÌNH - PROJECT

NHÀ Ở

HẠNG MỤC - PROJECT

XÂY MỚI

VỊ TRÍ - LOCATION

THỬA ĐẤT SỐ : 109, TỜ BẢN ĐỒ SỐ : 53
TỔ 4, P. NGỌC THỤY
Q. LONG BIÊN, TP. HÀ NỘI

GIÁM ĐỐC - DIRECTOR

ĐẶNG MINH ĐỨC

CHỦ TRÌ - PRIMARY ARCHITECT

TRẦN ĐỨC NGHĨA

KIỂM TRA / CHECKED BY

NGUYỄN PHƯƠNG THẢO

THIẾT KẾ / DESIGNED BY

NGUYỄN ĐĂNG KHOA

TÊN BẢN VẼ - DRAWING NAME

MẶT BẰNG TẦNG TUM

TỶ LỆ	BẢN VẼ SỐ - DRAWING NO
	KT- 04
NGÀY HOÀN THÀNH (DATE OF ISSUE)	DD/MM/-------